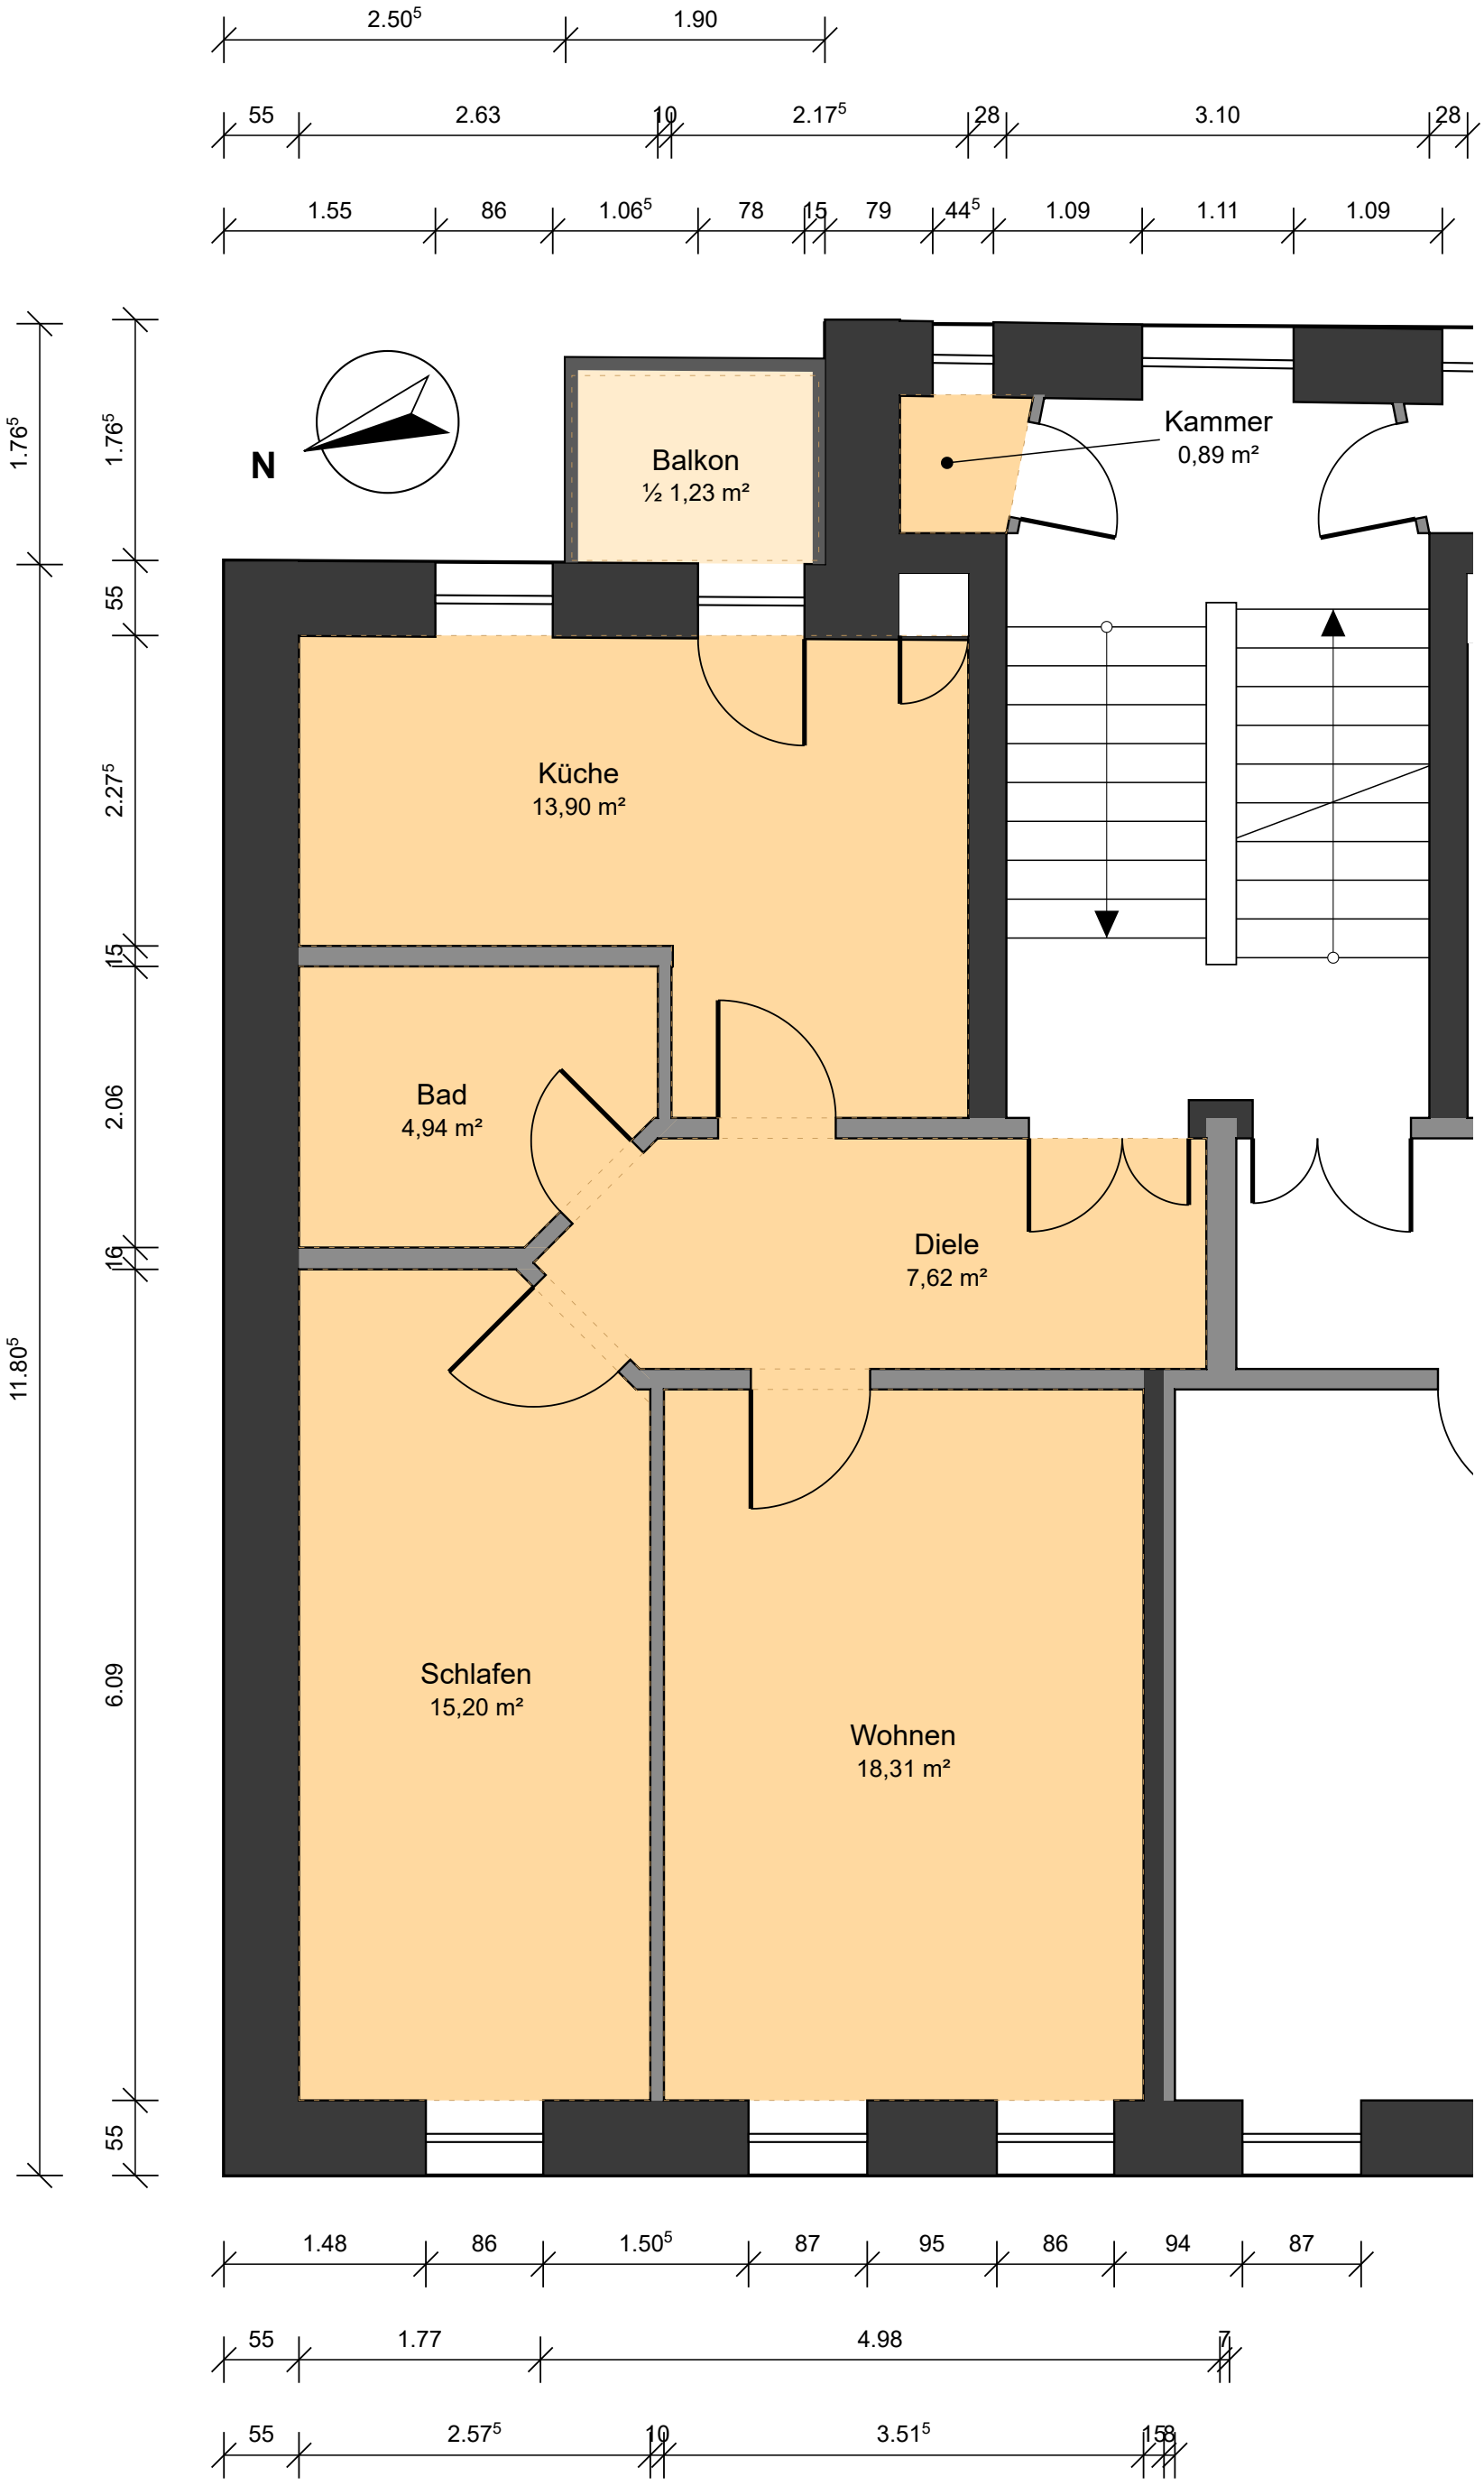

2.50⁵
1.90
55
2.63
10
2.17⁵
28
3.10
28
1.55
86
1.06⁵
78
15
79
44⁵
1.09
1.11
1.09
1.76⁵
1.76⁵
55
2.27⁵
15
2.06
16
11.80⁵
6.09
55
N
Balkon
½ 1,23 m²
Kammer
0,89 m²
Küche
13,90 m²
Bad
4,94 m²
Diele
7,62 m²
Schlafen
15,20 m²
Wohnen
18,31 m²
1.48
86
1.50⁵
87
95
86
94
87
55
1.77
4.98
7
55
2.57⁵
10
3.51⁵
15