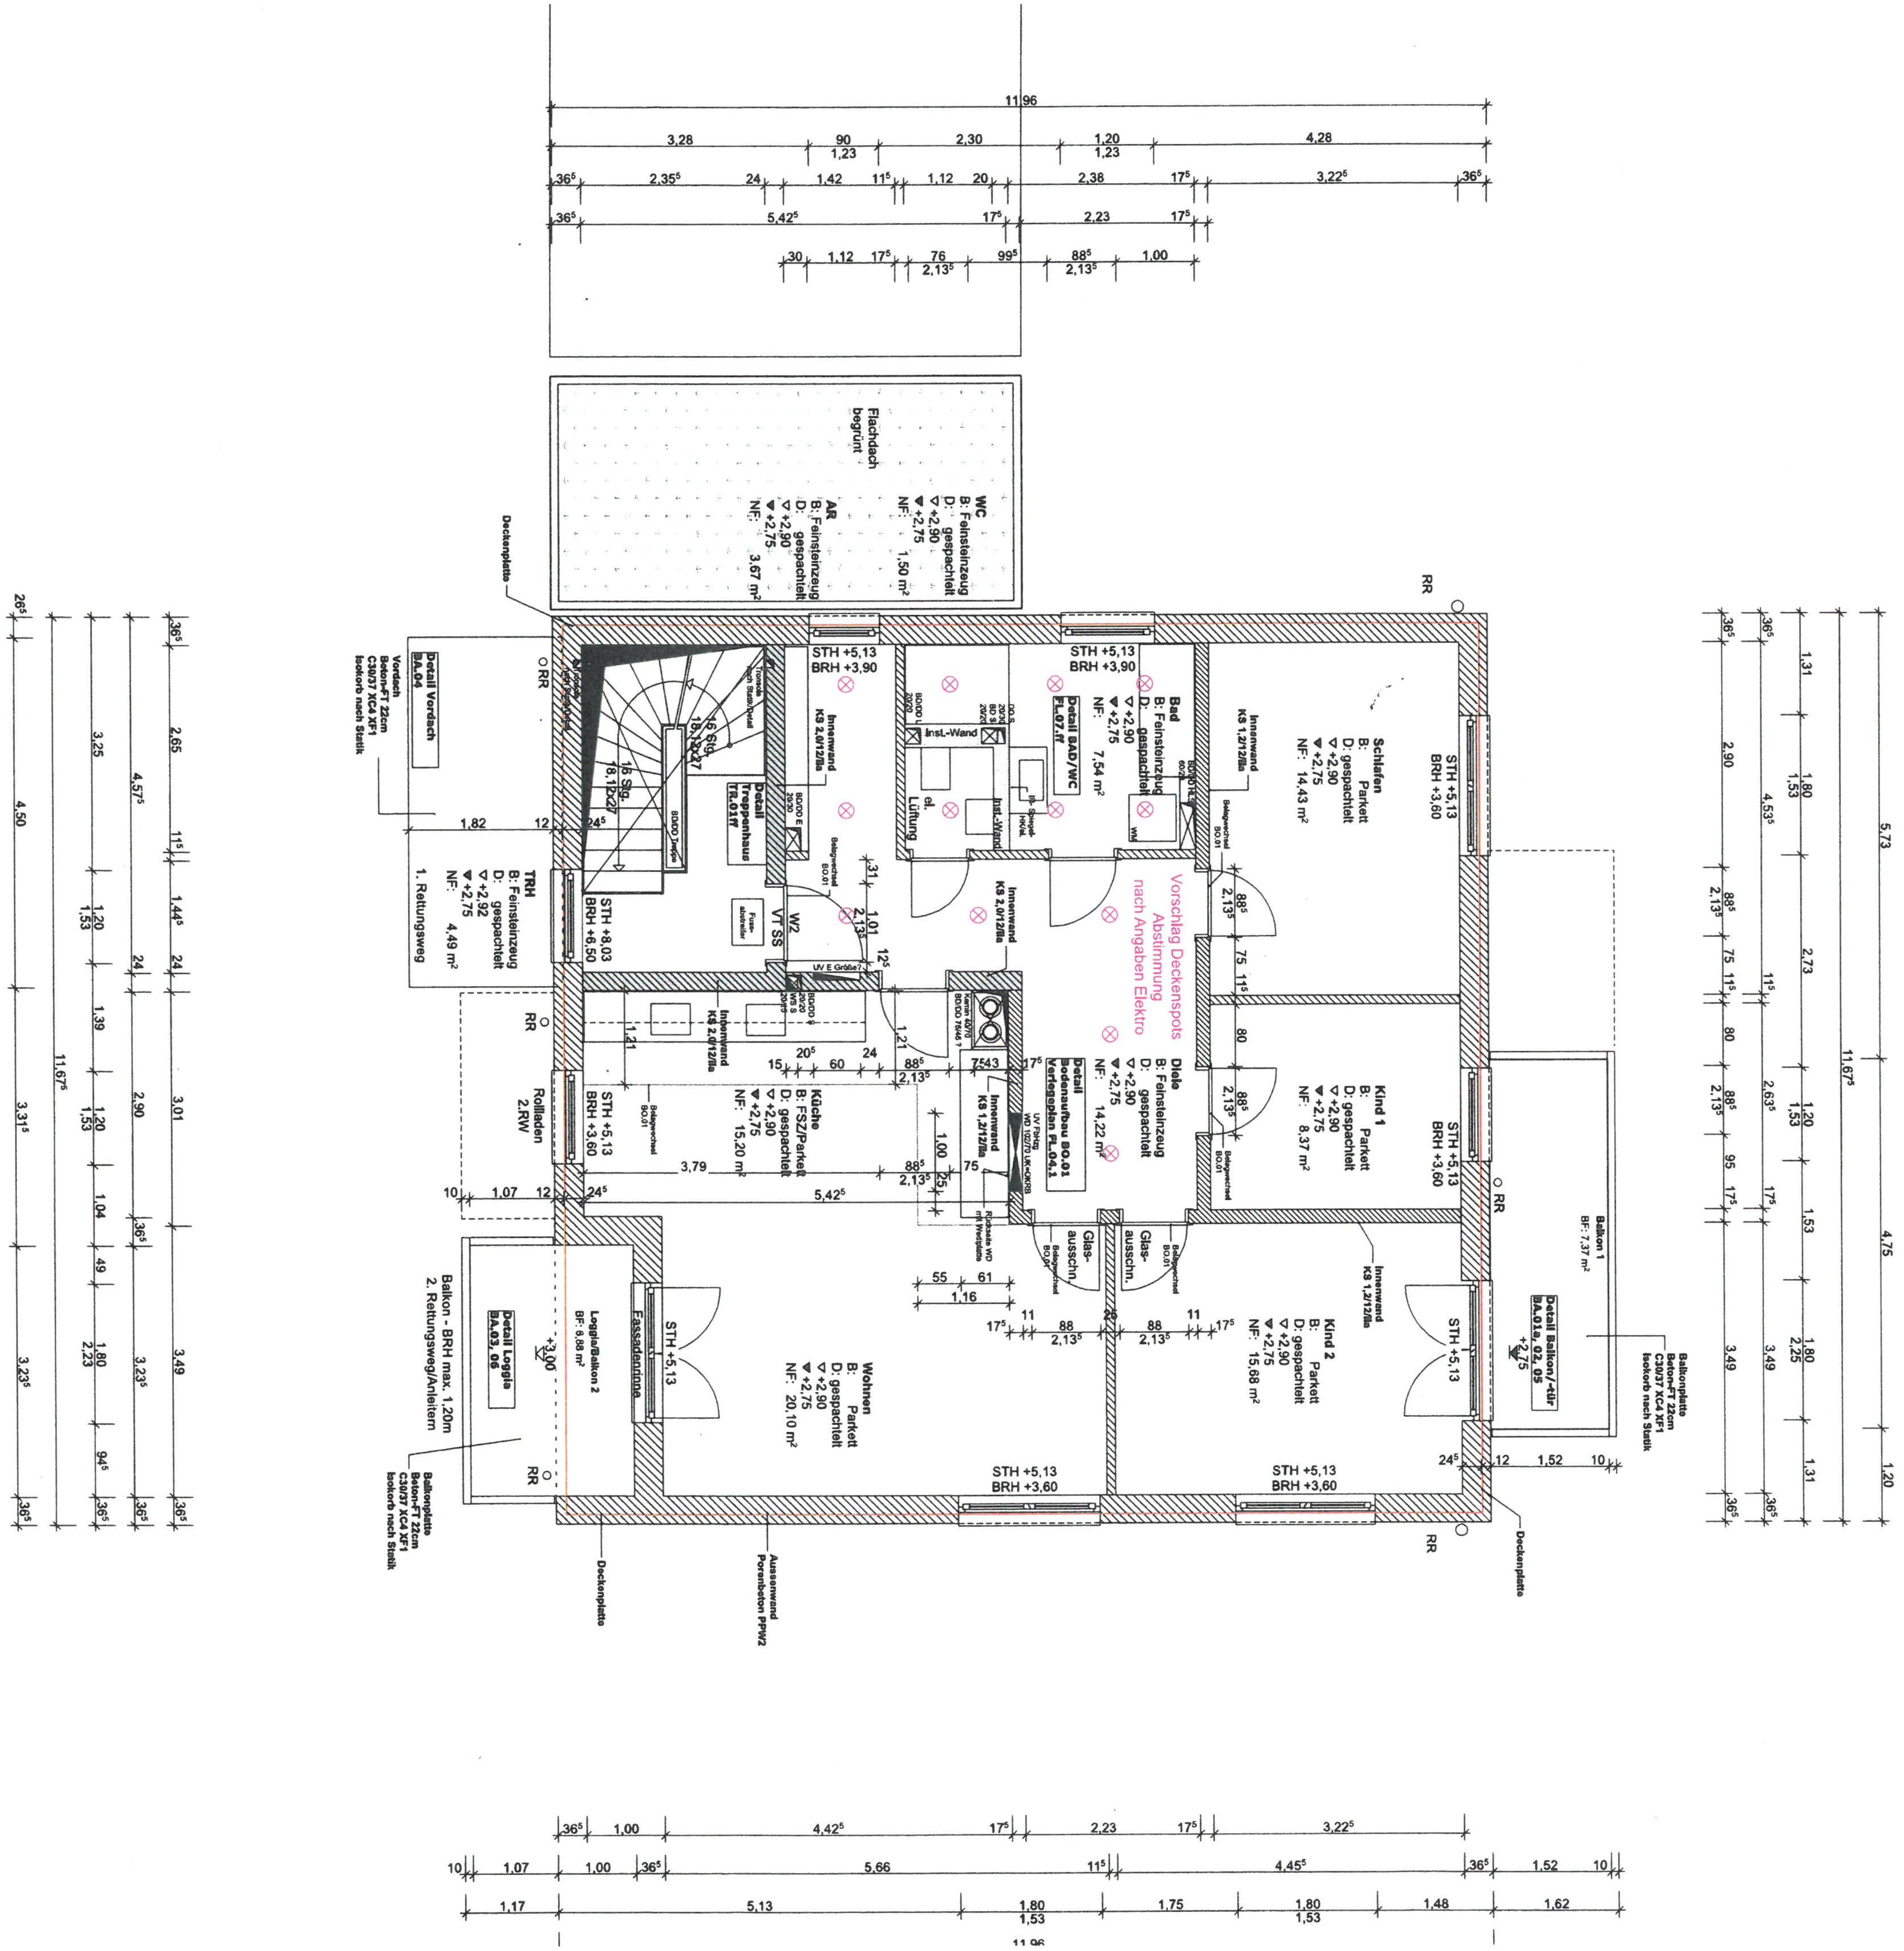
11,96
Flachdach begrünt
WC
B: Feinsteinzeug
D: gespachtelt
▽ +2,90
▼ +2,75
NF: 1,50 m²
AR
B: Feinsteinzeug
D: gespachtelt
▽ +2,90
▼ +2,75
NF: 3,67 m²
Deckenplatte
Detail Vordach BA.04
Vordach Beton-FT 22cm C30/37 XC4 XF1 isokorb nach Statik
Detail Treppenhaus TR.01ff
16 Stg. 18,1/26,7
Innenwand KS 2,0/12/IIa
STH +5,13
BRH +3,90
Bad
B: Feinsteinzeug
D: gespachtelt
▽ +2,90
▼ +2,75
NF: 7,54 m²
Detail BAD/WC FL.07.ff
Inst.-Wand
el. Lüftung
Schlafen
B: Parkett
D: gespachtelt
▽ +2,90
▼ +2,75
NF: 14,43 m²
STH +5,13
BRH +3,60
Innenwand KS 1,2/12/IIa
TRH
B: Feinsteinzeug
D: gespachtelt
▽ +2,92
▼ +2,75
NF: 4,49 m²
1. Rettungsweg
STH +8,03
BRH +6,50
VF SS
Vorschlag Deckenspots Abstimmung nach Angaben Elektro
Diele
B: Feinsteinzeug
D: gespachtelt
▽ +2,90
▼ +2,75
NF: 14,22 m²
Detail Bodenaufbau BO.01 Verlegeplan FL.04.1
Küche
B: FSZ/Parkett
D: gespachtelt
▽ +2,90
▼ +2,75
NF: 15,20 m²
STH +5,13
BRH +3,60
Rollladen 2.RW
Kind 1
B: Parkett
D: gespachtelt
▽ +2,90
▼ +2,75
NF: 8,37 m²
STH +5,13
BRH +3,60
Glas-ausschn.
Balkon 1
BF: 7,37 m²
Detail Balkon/-tür BA.01a, 02, 05
Balkonplatte Beton-FT 22cm C30/37 XC4 XF1 isokorb nach Statik
Wohnen
B: Parkett
D: gespachtelt
▽ +2,90
▼ +2,75
NF: 20,10 m²
STH +5,13
Loggia/Balkon 2
BF: 8,88 m²
Fassadenrinne
Detail Loggia BA.03, 06
Balkon - BRH max. 1,20m
2. Rettungsweg/Anleitern
Balkonplatte Beton-FT 22cm C30/37 XC4 XF1 isokorb nach Statik
Kind 2
B: Parkett
D: gespachtelt
▽ +2,90
▼ +2,75
NF: 15,68 m²
STH +5,13
BRH +3,60
STH +5,13
BRH +3,60
Aussenwand Porenbeton PPW2
Deckenplatte
RR