

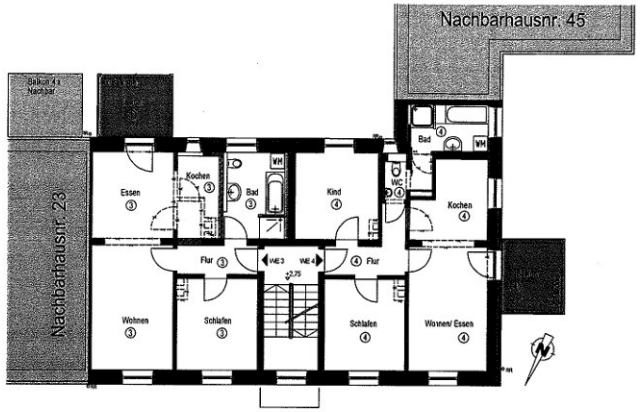



1. OBERGESCHOSS

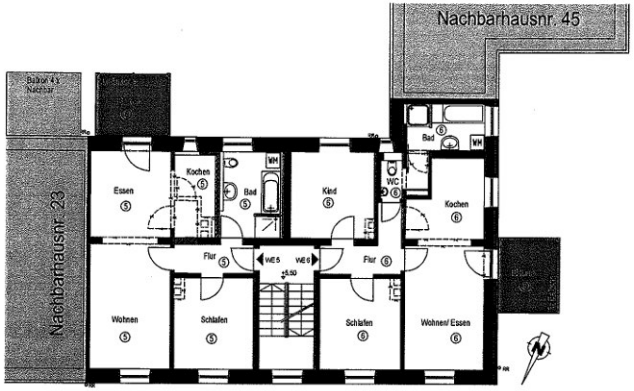


2. OBERGESCHOSS

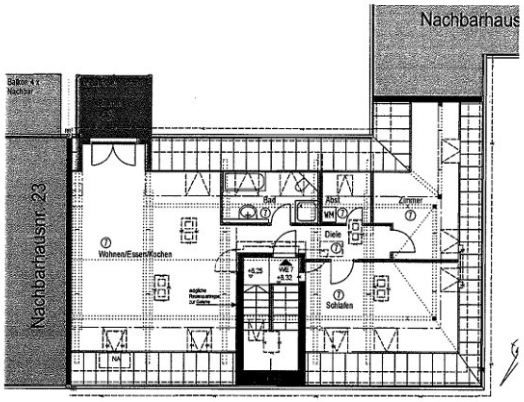

DACHGESCHOSS

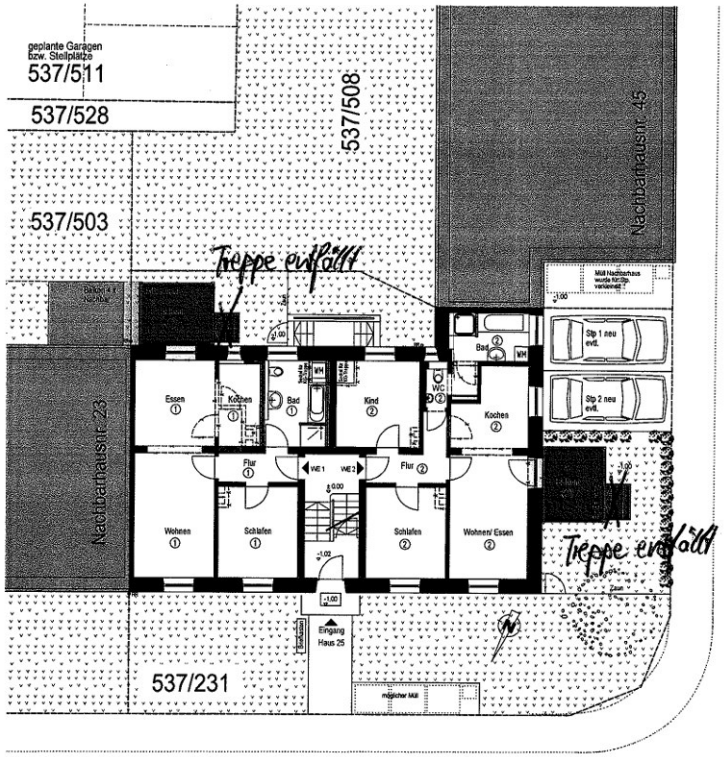

Dr.-Otto-Mayer-Straße

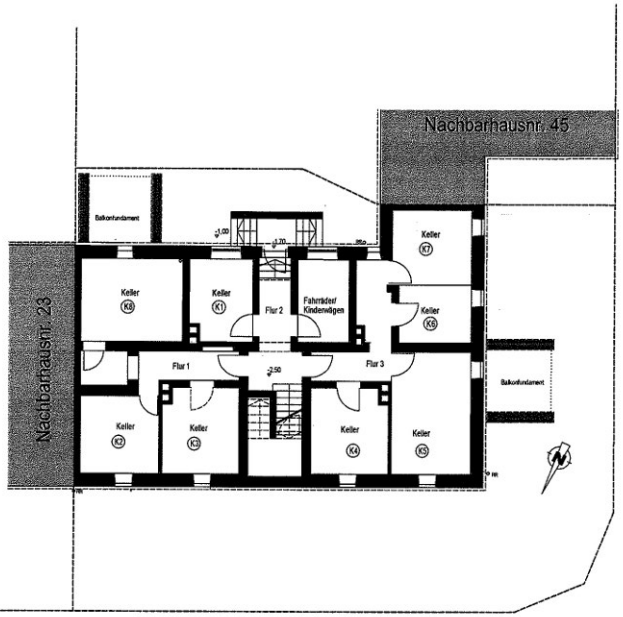

KELLERGESCHOSS

Reichenbachstraße

ERDGESCHOSS MIT AUSSENANLAGEN U. ABSTANDSFLÄCHEN


AUFTEILUNG
REICHENBACI

GRUNDI

PLANVERFASSE

A-TECK | ARCHITEKTUI
DIPL.ING. FH ARCHITEI
ANGELA SCHRÖCK
REISCHLESTRASSE 40
86153 AUGSBURG


MAßSTAB: 1:100

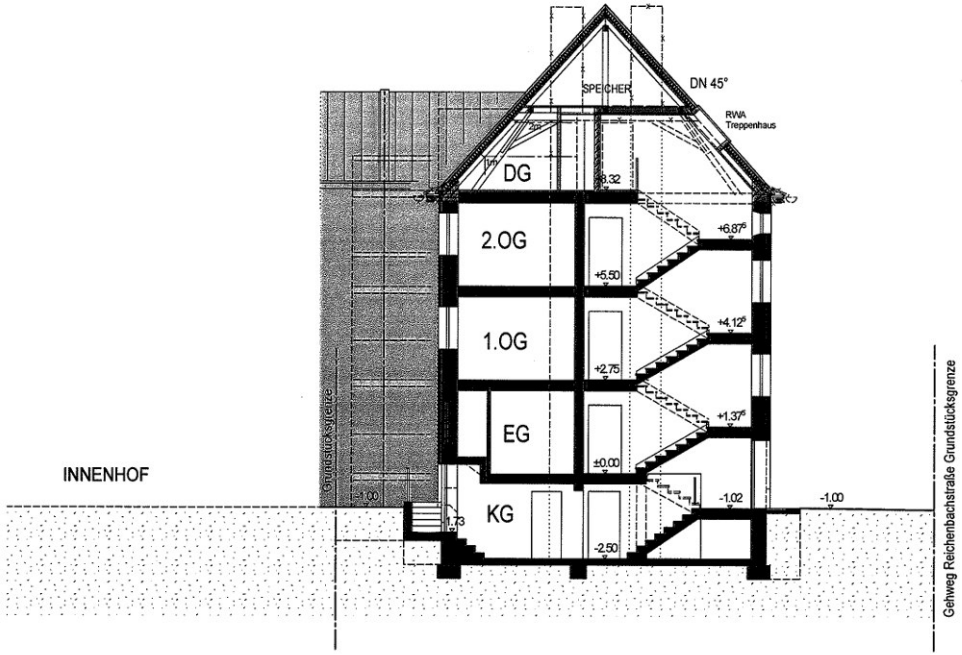


SCHNITT



WESTANSICHT

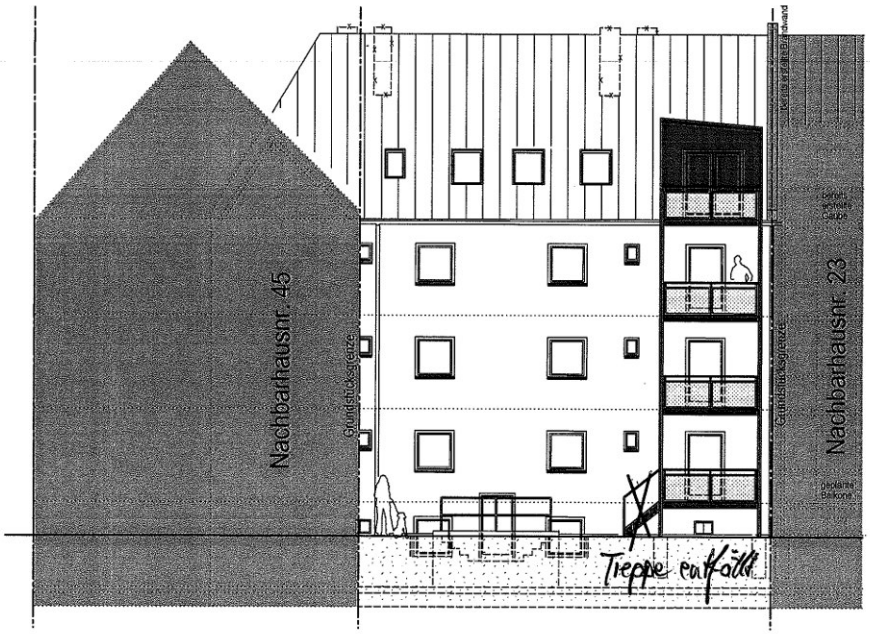

SÜDANSICHT / HOFANSICHT

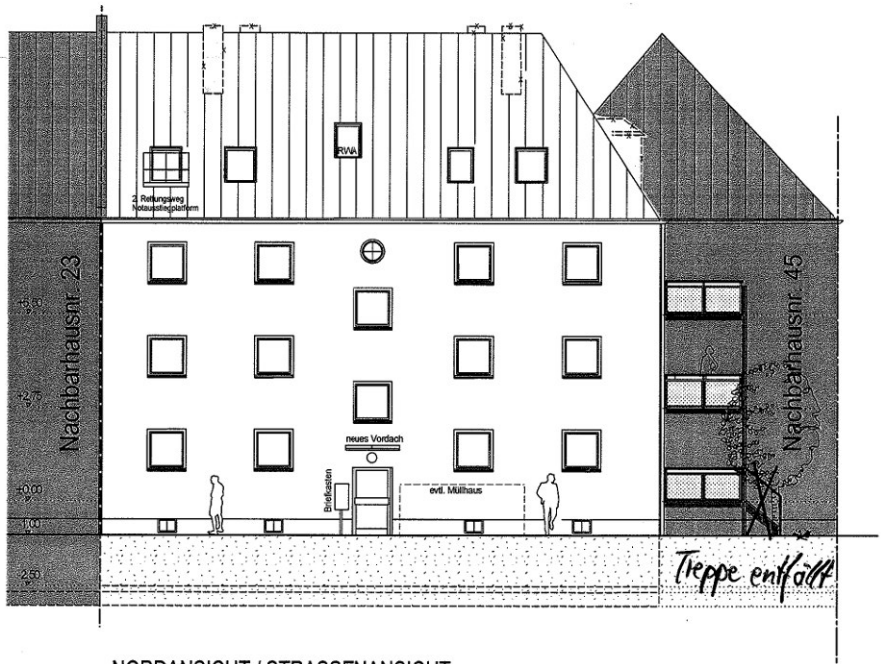

NORDANSICHT / STRASSENANSICHT

AUFTE
REICHE

SCH

PLANVE

A-TECK | A
DIPL.ING. I
ANGELA S
REISCHLE
86153 AUG